模型、空间与预算



轮廓面积 84.00 ㎡

净分区 80.5128 ㎡

总估算 180,288.72 元

预备费率 10%；预算余量 39,711.28 元

编号	空间	㎡
LOUNGE	客餐厅	32.25
COOK	厨房	12.38
PASS	横厅通道	11.34
SLEEP	卧室	11.76
WORK	独立书房	6.02
WASH	卫浴	6.76

预算 26 行，其中 21 行由模型规则计量。单价来源与计量口径见预算明细。

本案例为跨户型设计设定。图集由当前模型生成，尺寸单位mm；CAD模型空间1:1。

家具与空间平面



图面与模型

模型版本 v1.0

A3原幅比例 1:50

坐标X向东、Y向北，Z向上。

LOUNGE 客餐厅

COOK 厨房


PASS 横厅通道

SLEEP 卧室

WORK 独立书房

WASH 卫浴

地材与铺装意向

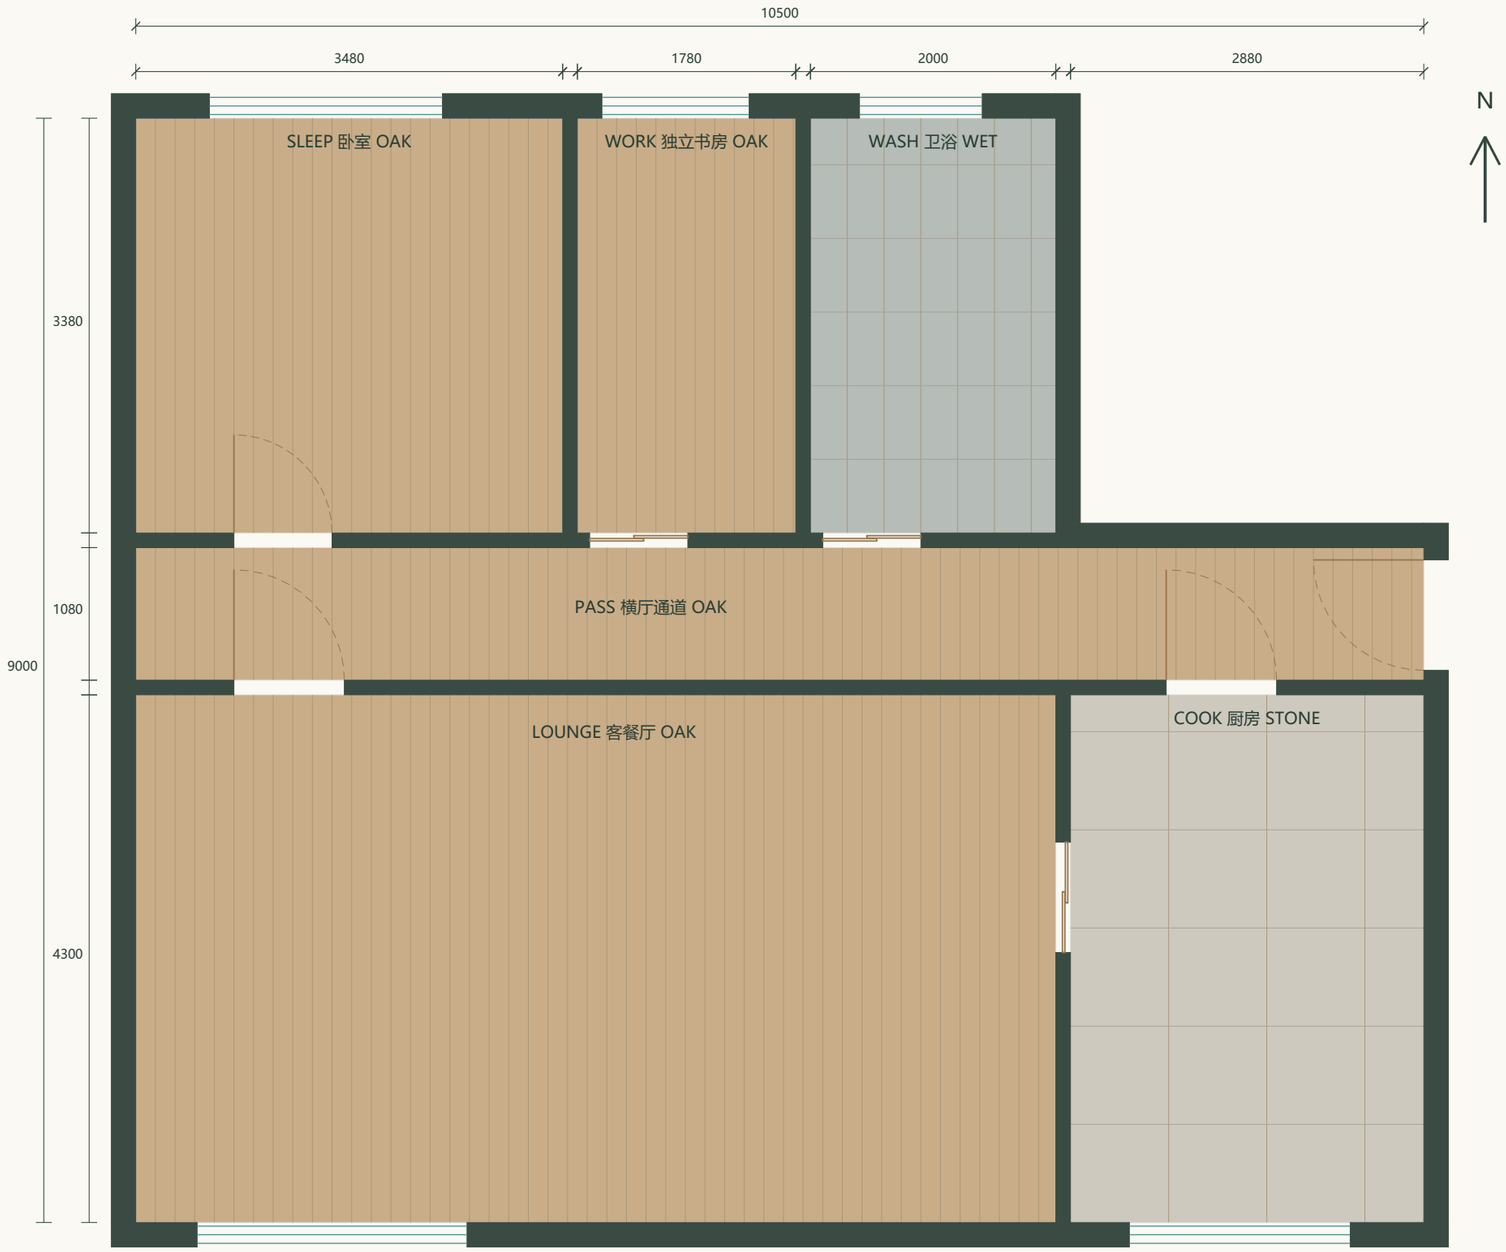

图面与模型

模型版本 v1.0

A3原幅比例 1:50

坐标X向东、Y向北，Z向上。

OAK 浅木复合地板

STONE 灰米厨房地砖

WET 浅灰卫浴砖

铺装间距来自材料pattern参数。

灯位与控制分组



图面与模型

模型版本 v1.0

A3原幅比例 1:50

坐标X向东、Y向北，Z向上。

10盏/条灯，6个分组。

虚线表达分组关系。

设备与机电条件



图面与模型

模型版本 v1.0


A3原幅比例 1:50

坐标X向东、Y向北，Z向上。

3项设备、4处条件点位。

点位z值自完成地面起。

定位与开口尺寸

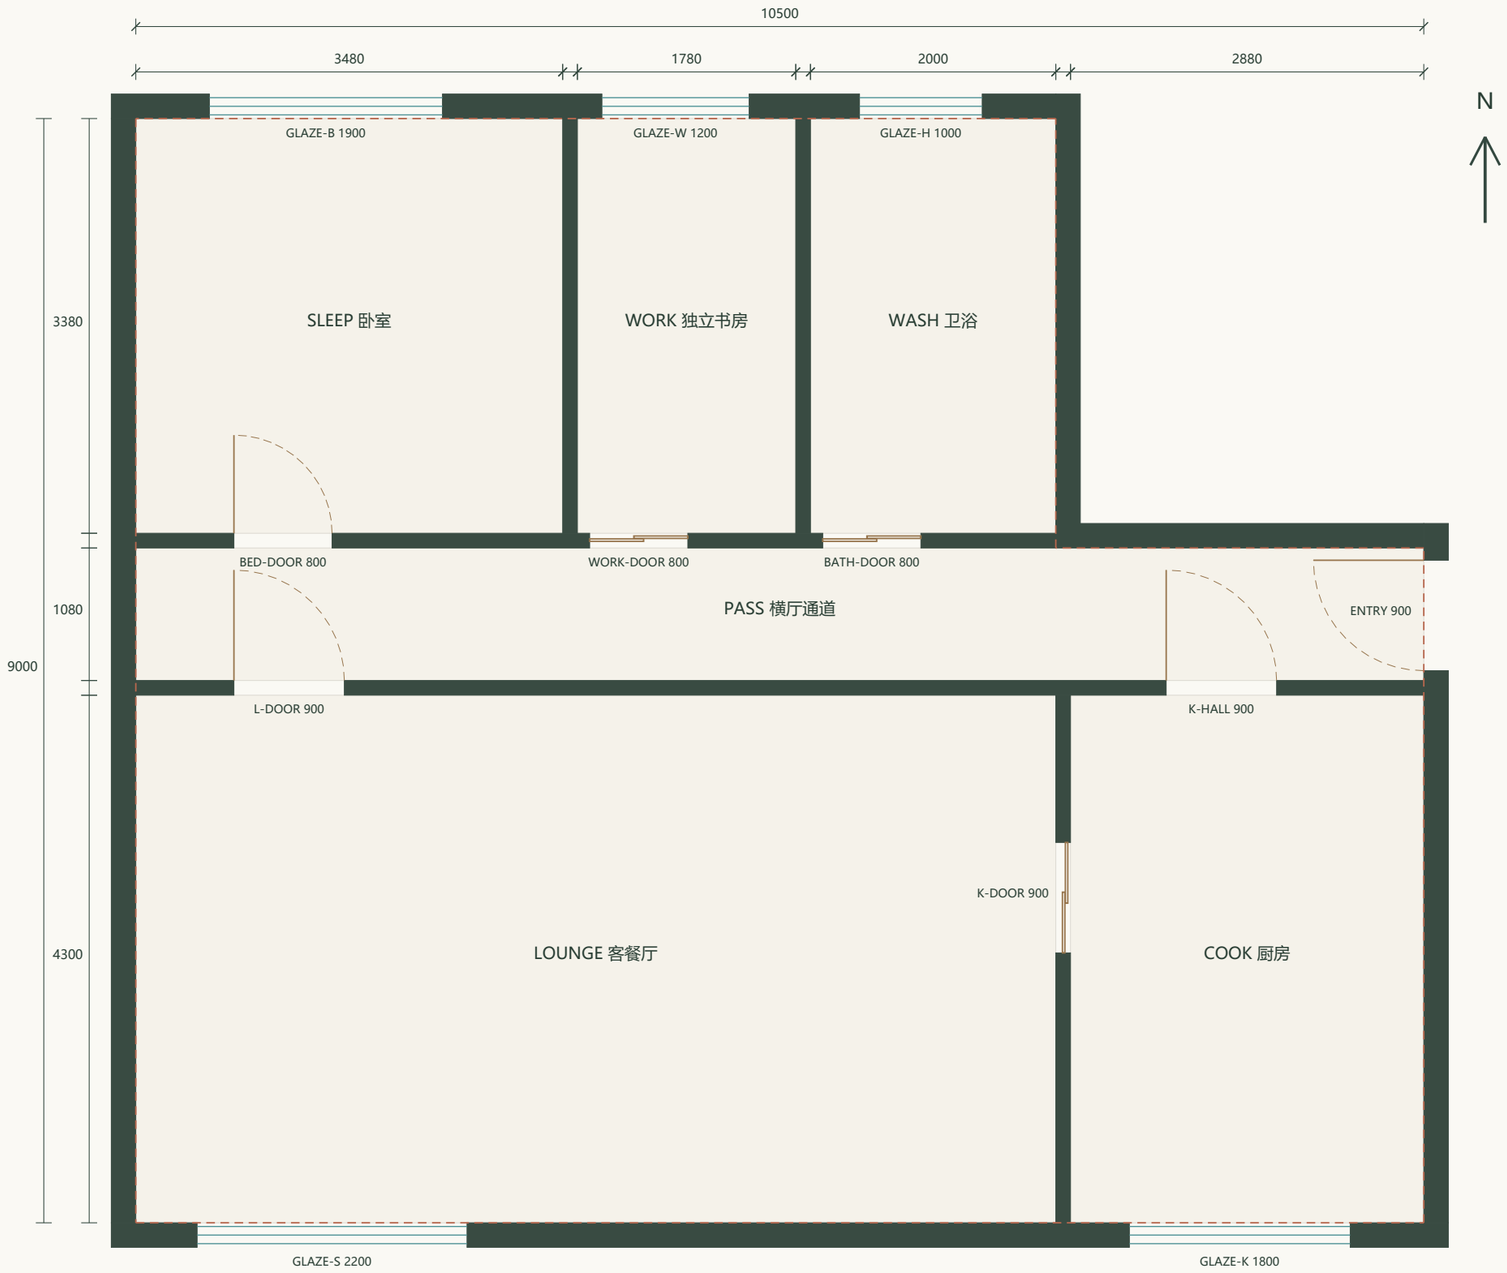

图面与模型

模型版本 v1.0

A3原幅比例 1:50

坐标X向东、Y向北，Z向上。


包围框 10500×9000 mm

实际轮廓面积 84.00㎡

红色虚线表达正交轮廓。


定制立面与剖面条件

CAB-A 卧室衣柜

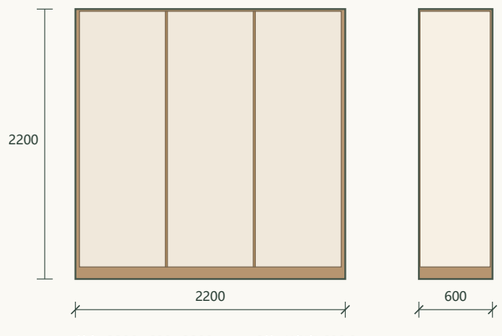


外包 2200×600×2200 mm；3格 / 净宽 699.3
板18 / 背9 / 踢脚80 / 单侧收口15 mm

KT-BASE 厨房地柜

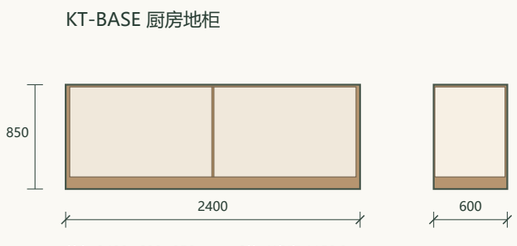

外包 2400×600×850 mm；2格 / 净宽 1158.0
板18 / 背9 / 踢脚80 / 单侧收口15 mm

SIDE-A 餐边柜

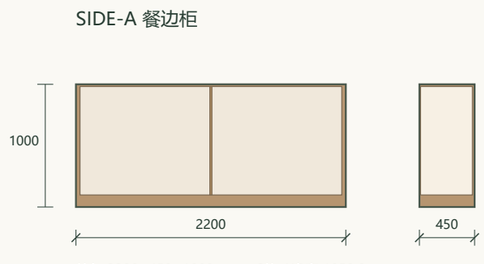

外包 2200×450×1000 mm；2格 / 净宽 1058.0
板18 / 背9 / 踢脚80 / 单侧收口15 mm

立剖为模型参数条件，柜内功能与五金另行选定。完整柜体见 joinery.csv。

图面与模型

模型版本 v1.0

A3原幅比例 1:50

坐标X向东、Y向北，Z向上。

立面、剖面由柜体参数生成。

选定柜体见图，全部柜体见清单。

柜内功能、设备开孔和五金另行深化。